



AVTOMOBIL
YO'LLARI
QO'MITASI


Каталог

выпускаемой продукции



O'ZYO'LKO'PRIK
KLASTERI
DAVLAT
MUASSASASI


Ташкент – 2024

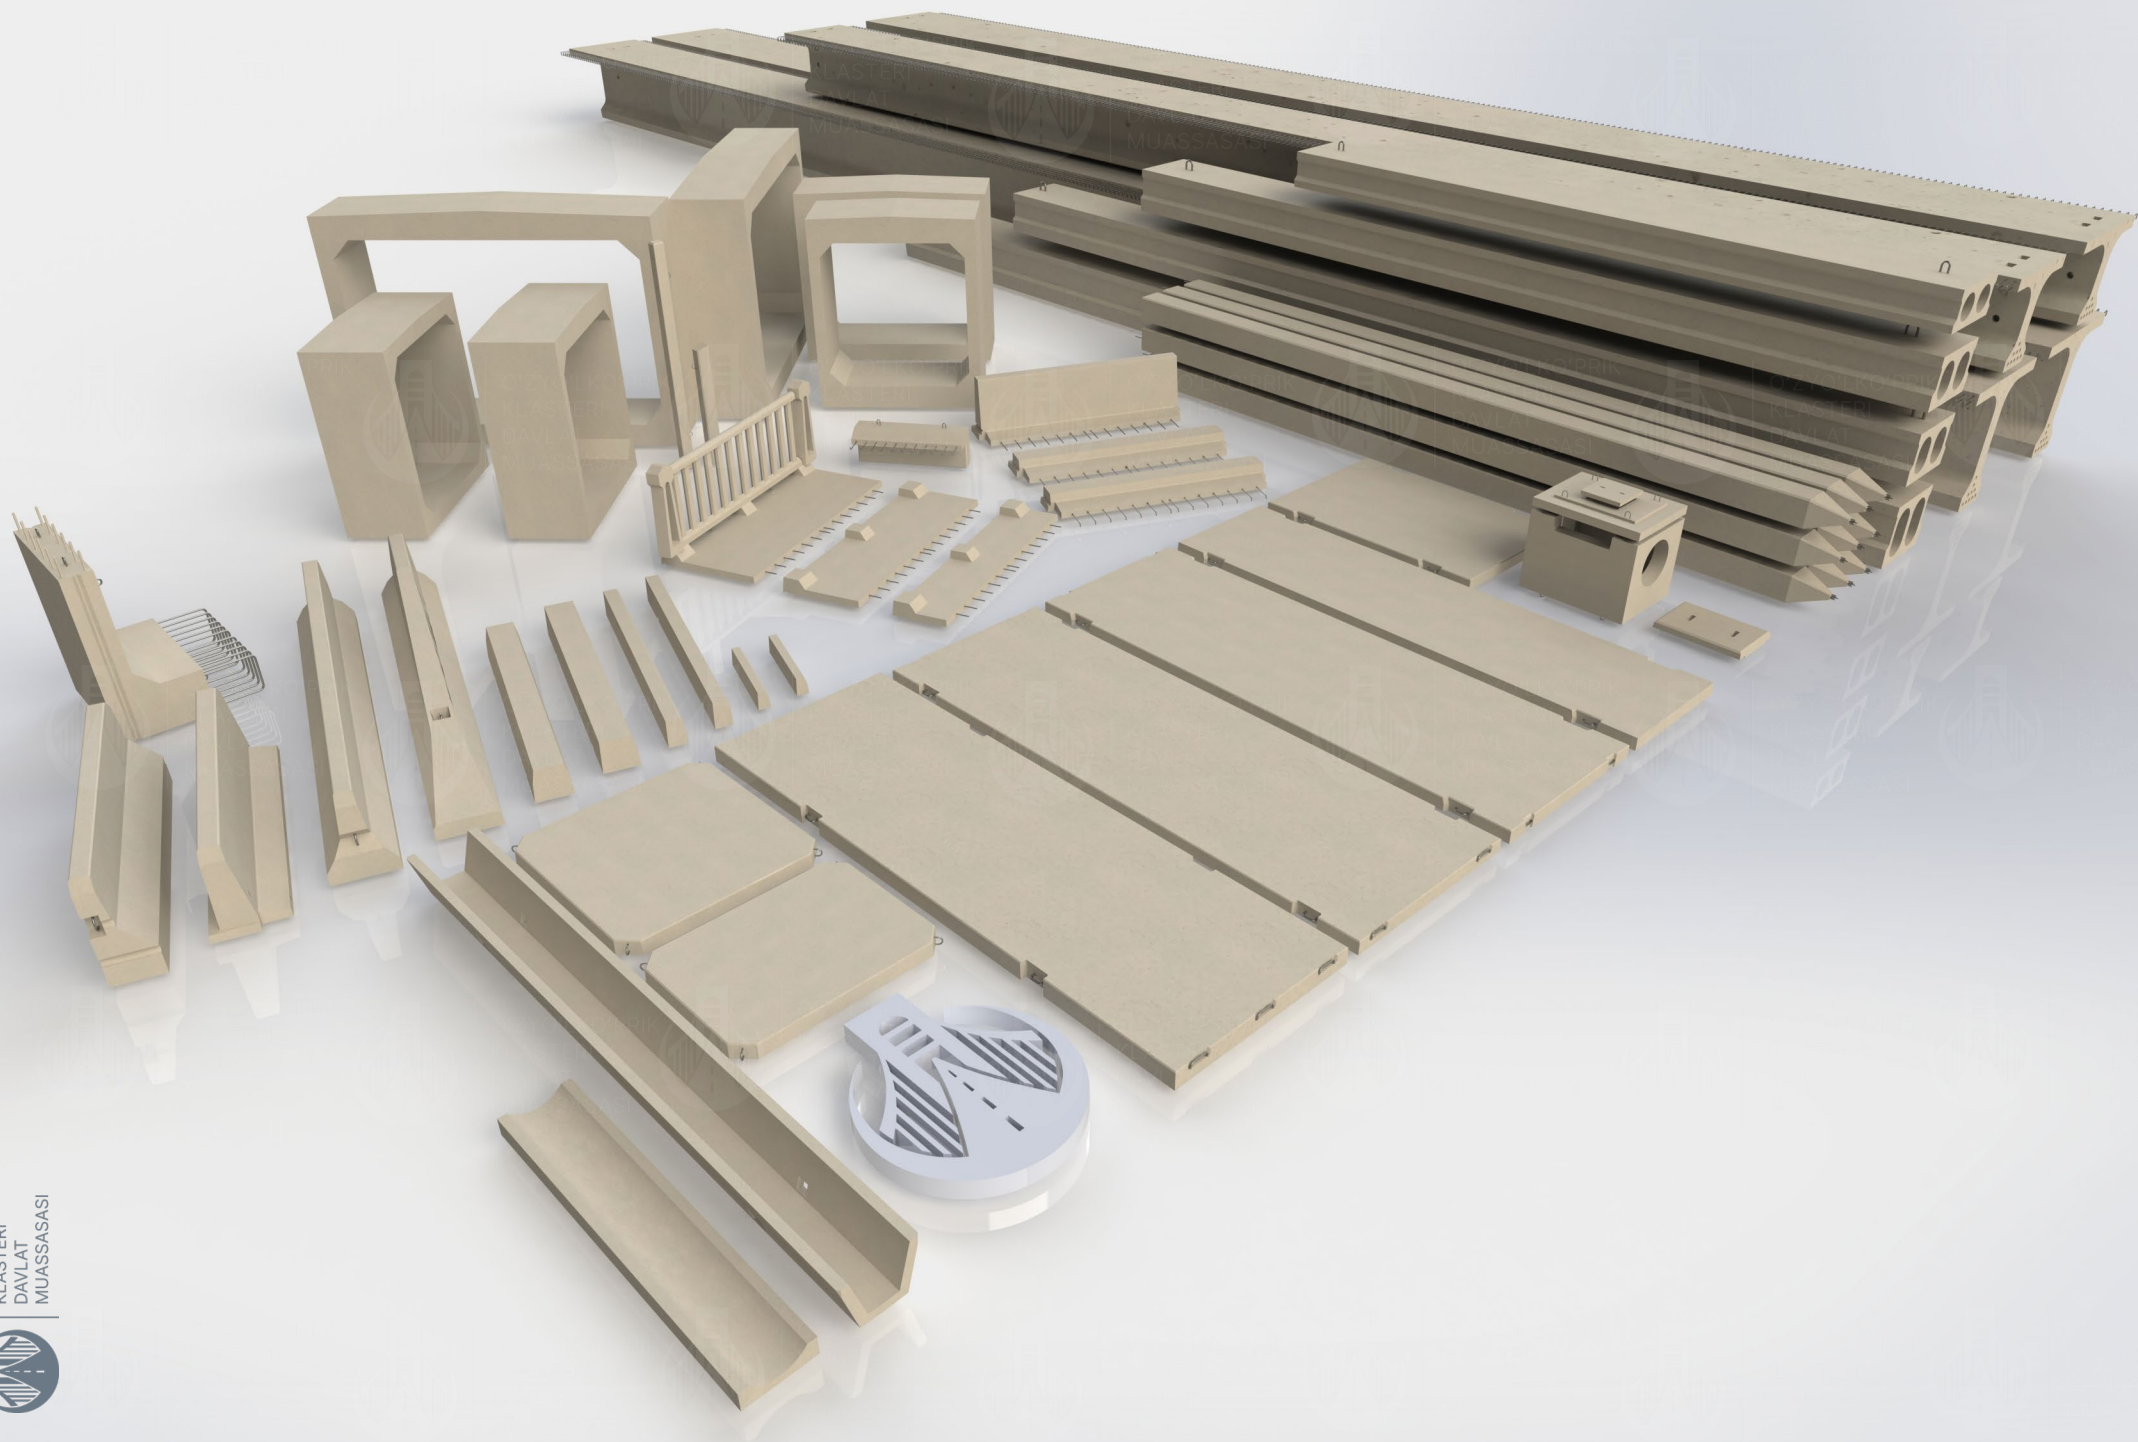

Балки пролетного строения			Блоки ограждения тротуаров	
2Б2400.174.120-9 В1400 А400	4		2ОТ-300.30.18	12
2Б2400.140.120-9 В1400 А400			2ОТ-300.30.18-П	
БЗ300.194.170-10 В1400 А400	5		3ОТ-100.30.19	
БЗ300.180.170-10 В1400 А400			3ОТ-200.30.19	
Плиты мостовые пустотные			3ОТ-300.30.19	
ПН 18.99.78 К-7	6		3ОТ-300.30.19-П	
ПН 15.99.63 К-7			4ОТ-100.20.13-1	
ПН 12.99.63 К-7			4ОТ-100.20.13-2	
ПН 9.99.48 К-7			Лотки железобетонные кюветные	
Плиты перекрытий			ЛК-6.6	13
2ПК*59.12-8А400-С9	7		ЛК-3.6	
2ПК*63.12-6А400-С9			ЛК-2.6	
Плита дорожная предварительно-напряжённая для аэродромных покрытий			ЛК-1.6	
ПАГ-14	8		ЛК-0,5,6	
ПАГ-18			ЛК-0,5,6	
Плита дорожная предварительно-напряжённая			Лотки прикромочные	
ПДНму 6.2.14	8		2ЛП-3.6	13
ПДОм 6.2.14			2ЛП-2.6	
ПДОм 6.0.75.14			2ЛП-1.6	
ПД 3.2.24-12			2ЛП-0,5,6	
ПД 3.2.24-14			Столбик сигнальный	
Плиты железобетонные тротуарные			СС-160.16.16	13
ПТК 2.2.14	8		Опора дорожных знаков	
ПТП-3.1,5.14			ОЖ-300.14.15	13
ПТП-3.2.14			ОЖ-400.14.15	
ПТП 6.1,5.14			Переходные плиты	
ПТП 6.2.14			ПП 8.99.45	14
Звенья железобетонные прямоугольных водопропускных труб			ПП 6.99.30	
ЗП 20.20.10-3 1 (Б-89А)	9-10		ПП 5.99.30	
ЗП 20.20.10-1 (Б-47)			ПП 4.99.30	
ЗП 20.20.10-2 (Б-48)			ПП 3.99.30	
ЗП 25.20.10-2 (Б-50)			ПП 3.200.24	
ЗП 40.25.10-1 (Б-94)			ПС 6.99.30	
ЗП 40.25.10-2 (Б-95)			Блоки опор мостов	
Сваи железобетонные призматические для мостовых опор			БО 1-5.100.49	14
СМ 6.35.1-А400; СМ 6.35.(1Т2-5Т7)-А400	11		Карнизный блок	
СМ 8.35.1-А400; СМ 8.35.(1Т2-5Т7)-А400			КБ 1.49.43.53	15
СМ 9.35.1-А400; СМ 9.35.(1Т2-5Т7)-А400			Блок железобетонный перильного ограждения	
СМ 10.35.1-А400; СМ 10.35.(1Т2-5Т7)-А400			БПО-14	15
СМ 12.35.1-А400; СМ 12.35.(1Т2-5Т7)-А400			СПО-14	
СМ 14.35.1-А400; СМ 14.35.(1Т3-5Т7)-А400			Блок колесоотбойный составного тротуарного блока	
Блоки дорожного ограждения			БК 3.55.75	15
1БДО-3.100.42-8	12		БК 3.55.15	
1БДО-3.100.42-10			БК 3.64.15	
1БДО-3.100.42-12			БК 3.64.75	
2БДО-5.84.60-8			БК 3.79.75	
2БДО-5.84.60-10			Плита тротуарная мостовая составного тротуарного блока	
2БДО-5.84.60-12			ПТМ 3.68.8	15
2БДО-5.84.60-К			ПТМ 3.100.8	
3БДО-3.83.64			ПТМ 3.130.8	
Блоки ограждения разделительной полосы			Комплекс дренажной системы	
ЗРП-300.35.36	12		КД 130.100.95	16
4РП-300.35.36			ККД 130.100.13	
			ПТК 0,5,0,5,5	
			КЛ 100.68.10	
			Примечание	17





Балки пролетного строения длиной
24 м цельноперевозимые с
натяжением на упоры для
автодорожных мостов

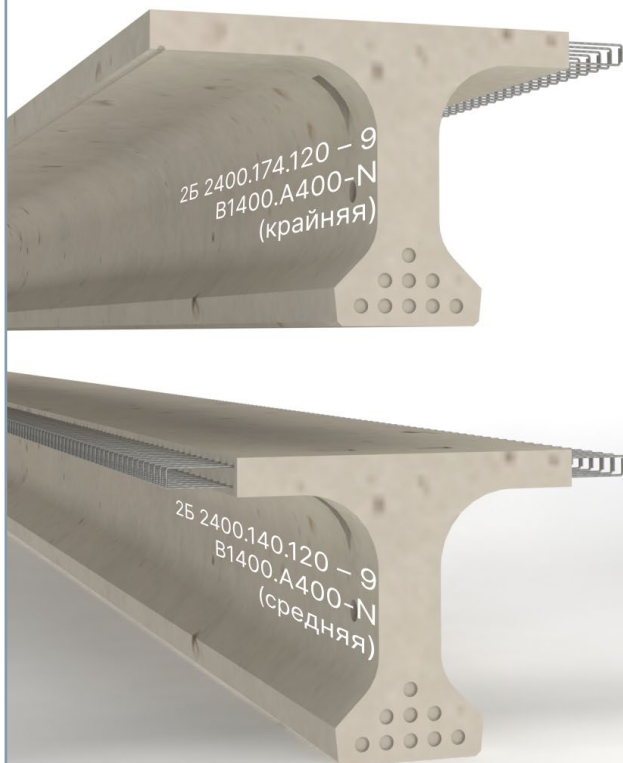

Габаритные размеры	Марка	2Б 2400.174.120 – 9 В1400.А400-Н (крайняя)	2Б 2400.140.120 – 9 В1400.А400-Н (средняя)	1
	Длина (mm)	24000	24000	2
	Ширина (mm)	1740	1400	3
	Высота (mm)	1200	1200	4
Об изделии	Балка двутаврового сечения цельноперевозимая для автодорожных мостов предварительно-напряжённая крайняя на автомобильных дорогах общего пользования. Предварительно напряжённая с натяжением арматуры на упоры стенда, предназначена для эксплуатации в районах с сейсмичностью до 9 баллов.			5
	Рабочая документация	Т.П 3.503.1-81.UZ Доп.3Д к вып. 5-5		6
	Нормативная документация	O'z DSt 2844:2019		7
	Технологическая документация	ТИ 02162770-09:2014		8
Свойства	Нормативная нагрузка	А 14, НК 100		9
	Бетон тяжелый	ГОСТ 26633-2012		10
	Плотность бетона (kg/m³)	от 2200 до 2500		11
	Класс бетона по прочности на сжатие	В 35		12
	Отпускная прочность (%)	80		13
	Морозостойкость	F 200		14
	Марка по водонепроницаемости	W 6		15
	Объем бетона (m³)	14.58	13.36	16
	Масса балки (t)	36.4	33.1	17
	Ø5 (напрягаемая, 9 пучков из 24 проволок)	999.0		18
Масса арматуры (kg)	Ø4 ВI	5.35		19
	Ø6.5 А240	100.86		20
	Ø8 А400	463.58	435.01	21
	Ø12 А240	5.11		22
	Ø16 А240	7.68		23
	Ø10 А400	560.24	601.98	24
	Ø12 А400	740.95	818.69	25
	Полосовая сталь (звёздочка): 10x80x80	7.20		26
	Полосовая сталь (МН-6): 10x40x50	2.56		27
	Полосовая сталь (МН-6): 10x200x250	15.72		28
А	Б	В	Г	



Балки пролетного строения длиной 33 м цельноперевозимые с натяжением на упоры для автодорожных мостов

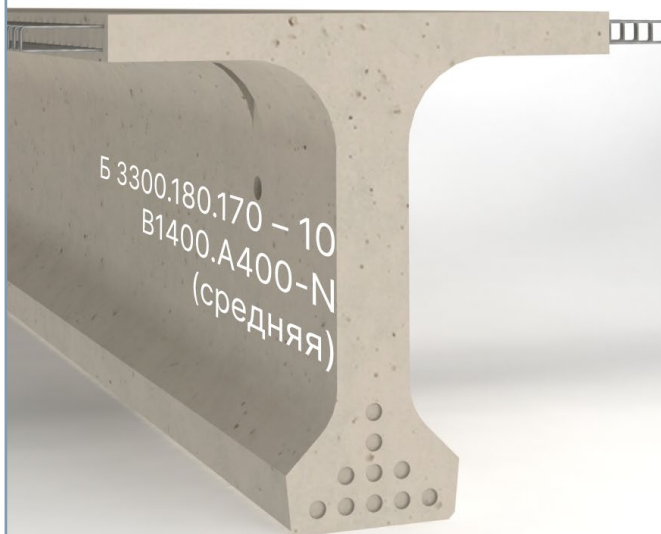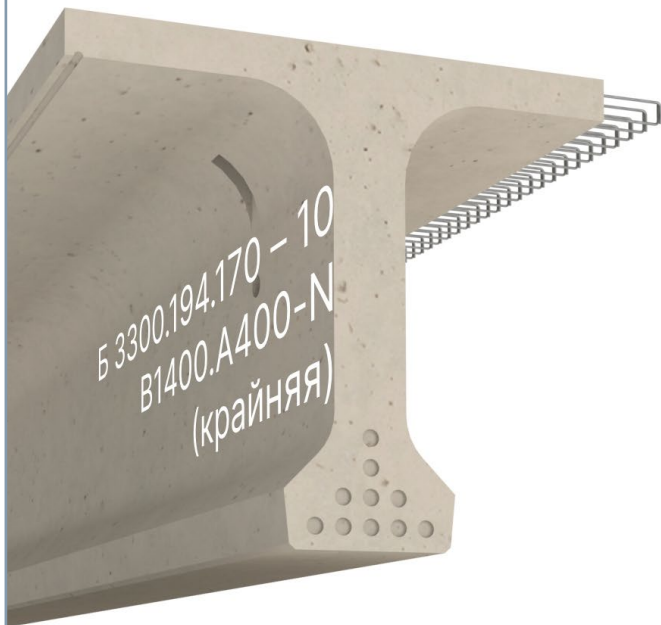

Габаритные размеры	Марка	Б 3300.194.170 – 10 В1400.А400-Н (крайняя)	Б 3300.180.170 – 10 В1400.А400-Н (средняя)	1
	Длина (mm)	33000	33000	2
	Ширина (mm)	1940	1800	3
	Высота (mm)	1700	1200	4
Об изделия	Балка двутаврового сечения цельноперевозимая для автодорожных мостов предварительно-напряжённая крайняя на автомобильных дорогах общего пользования. Предварительно напряжённая с натяжением арматуры на упоры стенда, предназначена для эксплуатации в районах с сейсмичностью до 9 баллов.			5
	Рабочая документация	Т.П 3.503.1-81выпуск 5-6		6
	Нормативная документация	O'z DSt 2844:2019		7
	Технологическая документация	ТИ 02162770-31:2024		8
Свойства	Нормативная нагрузка	А 14, НК 100		9
	Бетон тяжелый	ГОСТ 26633-2012		10
	Плотность бетона (kg/m³)	от 2200 до 2500		11
	Класс бетона по прочности на сжатие	В 35		12
	Отпускная прочность (%)	75		13
	Морозостойкость	F 200		14
	Марка по водонепроницаемости	W 6		15
	Объем бетона (m³)	24.48	23.78	16
	Масса балки (t)	61.2	59.5	17
Масса арматуры (kg)	Ø5 (напрягаемая, 9 пучков из 24 проволок)	1441.44		18
	Ø4 ВI	5.94		19
	Ø6.5 А240	126.97		20
	Ø8 А400	643.45	621.63	21
	Ø12 А240	5.68		22
	Ø16 А240	8.53		23
	Ø10 А400	871.17	1027.58	24
	Ø12 А400	979.61	1144.74	25
	Полосовая сталь (звёздочка): 10х80х80	8.0		26
	Полосовая сталь (МН-6): 10х40х50	5.12	31.44	27
	Полосовая сталь (МН-6): 10х200х250	-		28
А	Б	В	Г	




Плиты пустотные железобетонные
предварительно-напряженные для
автодорожных мостов



Габаритные размеры	Марка	ПН 9.99.48 К-7	ПН 12.99.63 К-7	ПН 15.99.63 К-7	ПН 18.99.78 К-7	1
	Длина (mm)	9000	12000	15000	18000	2
	Ширина (mm)	990	990	990	990	3
	Высота (mm)	480	630	630	780	4
Об изделия	Пустотная плита для мостов и путепроводов на автомобильных дорогах, эксплуатируется в районах с сейсмичностью до 9 баллов включительно. Предварительно напряжённый железобетон с натяжением арматуры на упоры форм.					5
	Рабочая документация	ТП.3.503-12 UZ доп. к Вып. 16 «И»				6
	Нормативная документация	O'z DSt 2838:2019				7
	Технологическая документация	ТИ 02162770-26:2014	ТИ 02162770-27:2014		ТИ 02162770-29:2014	8
Свойства	Нормативная нагрузка	А 14, НК 100				9
	Бетон тяжелый	ГОСТ 26633-2012				10
	Плотность бетона (kg/m³)	от 2200 до 2500				11
	Класс бетона по прочности на сжатие	В 35				12
	Отпускная прочность (%)	80				13
	Морозостойкость	F 200				14
	Объем бетона (m³)	2.5	4.2	5.2	7.0	15
	Масса плиты (t)	6.3	10.4	12.9	17.5	16
Масса арматуры (kg)	Ø15 К-7 (напрягаемая)	96.7	133.5	217.6	300.0	17
	Ø6 А240	40.5	91.5	125.7	166.1	18
	Ø8 А240	58.2	58.2	58.2	58.2	19
	Ø10 А400	46.8	55.4	55.4	31.0	20
	Ø22 А240	10.7	-	-	-	21
	Ø28 А240	-	15.4	-	-	22
	Ø32 А240	-	-	20.3	-	23
	Ø36 А240	-	-	-	63.2	24
	Проволока вязальная	-	0.3	0.3	0.5	25
	Полоса стальная σ=18 мм	-	4.6	4.6	4.6	26
А	Б	В	Г	Д	Е	



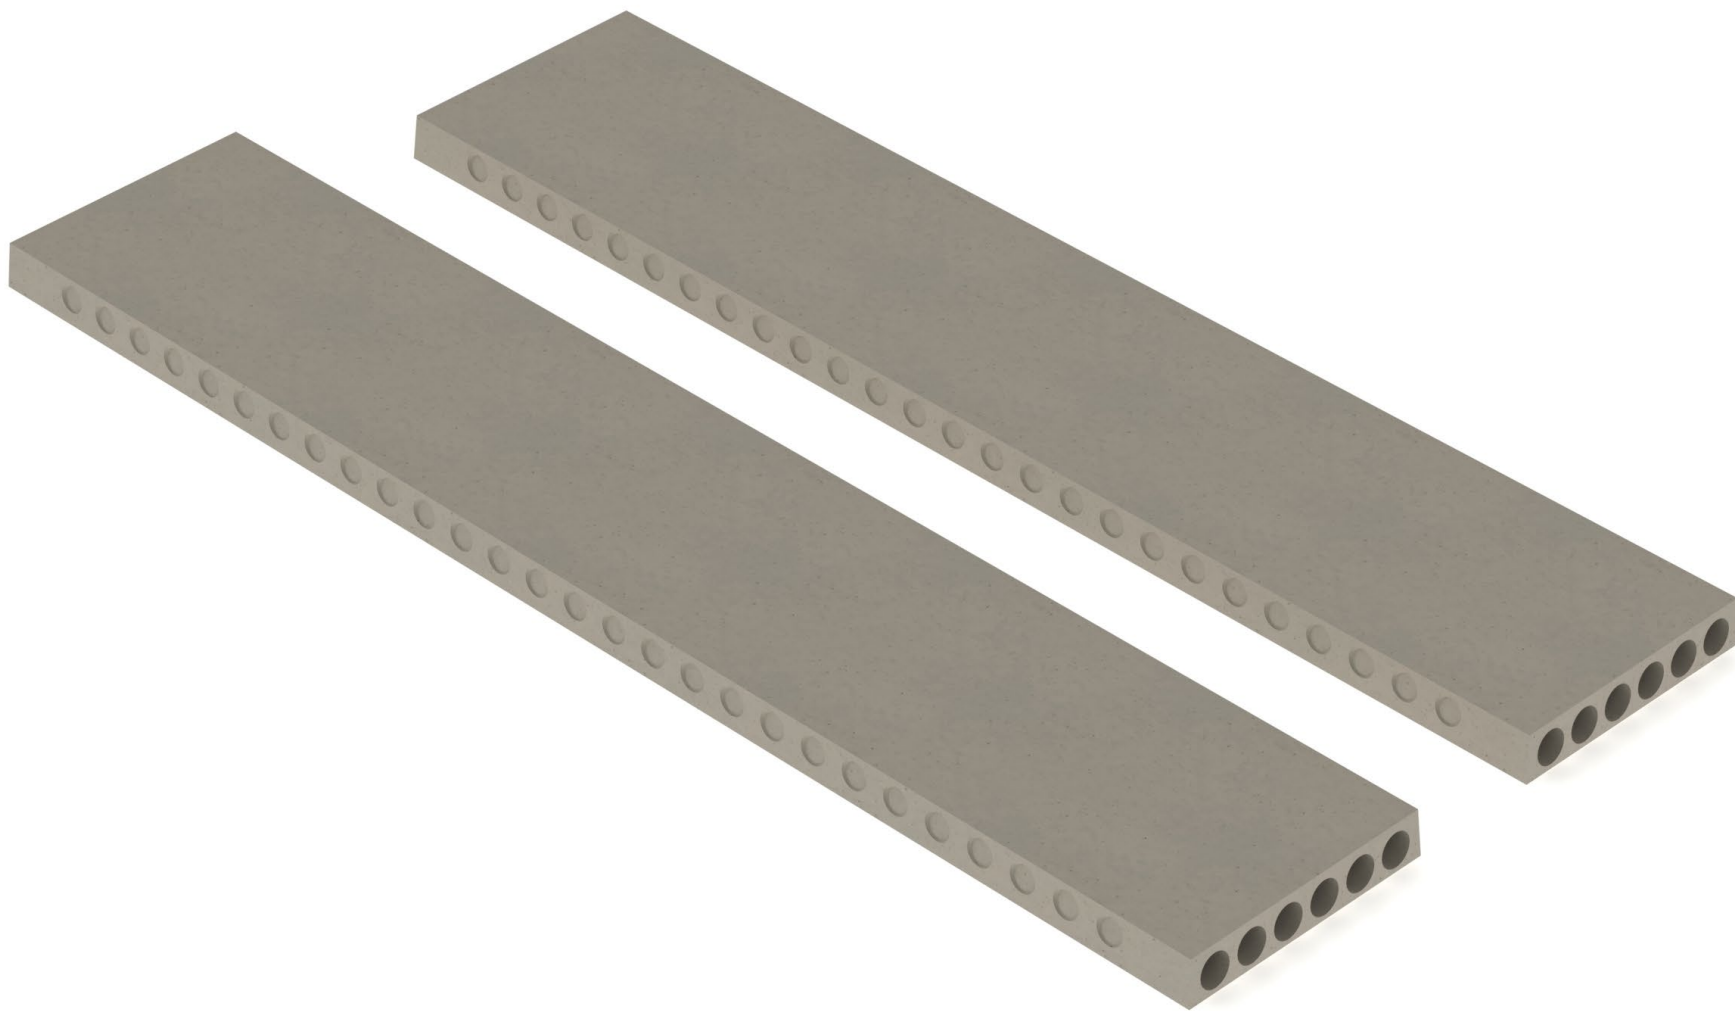

№	Наименование конструкции	Марка конструкции	Обозначение нормативного документа	Объём бетона (м³)	Масса (t)	Габаритные размеры (mm)	Класс бетона по прочности на сжатие	Марка по морозостойкости, не менее	Марка по водонепроницаемости, не менее	Плотность бетона (kg/m³)	Нормативная отпускная прочность бетона, лето/зима (%)
А	Б	В	Г	Д	Е	Ж	З	И	К	Л	М
1	Плиты перекрытий железобетонные многопустотные предварительно напряжённые армированные стержнями из стали класса А400 для строительства жилых и общественных зданий	2ПК*59.12-8А400-С9	ГОСТ 9561-2016	0.95	2.38	5860x1190x220	В25	F75			70/85
2		2ПК*63.12-6А400-С9		1.03	2.55	6280x1190x220					

ПТП-3.2.14

ПТП 6.1,5.14

ПТП 6.2.14

ПАГ-14


ПАГ-18

ПТП 2.1,5.14

ПТК 2.2.14

№	Наименование конструкции	Марка конструкции	Обозначение нормативного документа	Объём бетона (м³)	Масса (t)	Габаритные размеры (mm)	Класс бетона по прочности на сжатие	Марка по морозостойкости, не менее	Марка по водонепроницаемости, не менее	Плотность бетона (kg/m³)	Нормативная отпускная прочность бетона, лето/зима (%)
А	Б	В	Г	Д	Е	Ж	З	И	К	Л	М
1	Плиты железобетонные для аэродромных покрытий	ПАГ-14	ГОСТ 25912.1-91	1.68	4.20	6000x2000x140	B25	F200	W6	2200-2500	80
2		ПАГ-18	ГОСТ 25912.2-91	2.16	5.40	6000x2000x180					
3	Плиты железобетонные дорожные	ПДНму 6.2.14	O'z DSt 3411:2019	1.68	4.20	6000x2000x140	B27,5	F200	W6	2200-2500	80
4		ПДОм 6.2.14		1.68	4.20	6000x2000x140					
5		ПДОм 6.0.75.14		0.63	1.58	6000x750x140					
6	Плиты бетонные дорожные	ПД 3.2.24-12	O'z DSt 3169:2017	1.44	3.46	2980x2000x240	B30	F200	W4	2200-2500	80
7		ПД 3.2.24-14									
8	Плиты железобетонные для обустройства тротуаров	ПТК 2.2.14	O'z DSt-3030:2021	0.56	1.38	2000x2000x140	B27,5	F200	W4	2200-2500	70/80
9		ПТП 2.1,5.14		0.42	1.05	2000x1496x140					
10		ПТП-3.2.14		0.84	2.10	3000x2000x140					
11		ПТП 6.1,5.14		1.26	3.15	6000x1500x140					
12		ПТП 6.2.14		1.68	4.20	6000x2000x140					




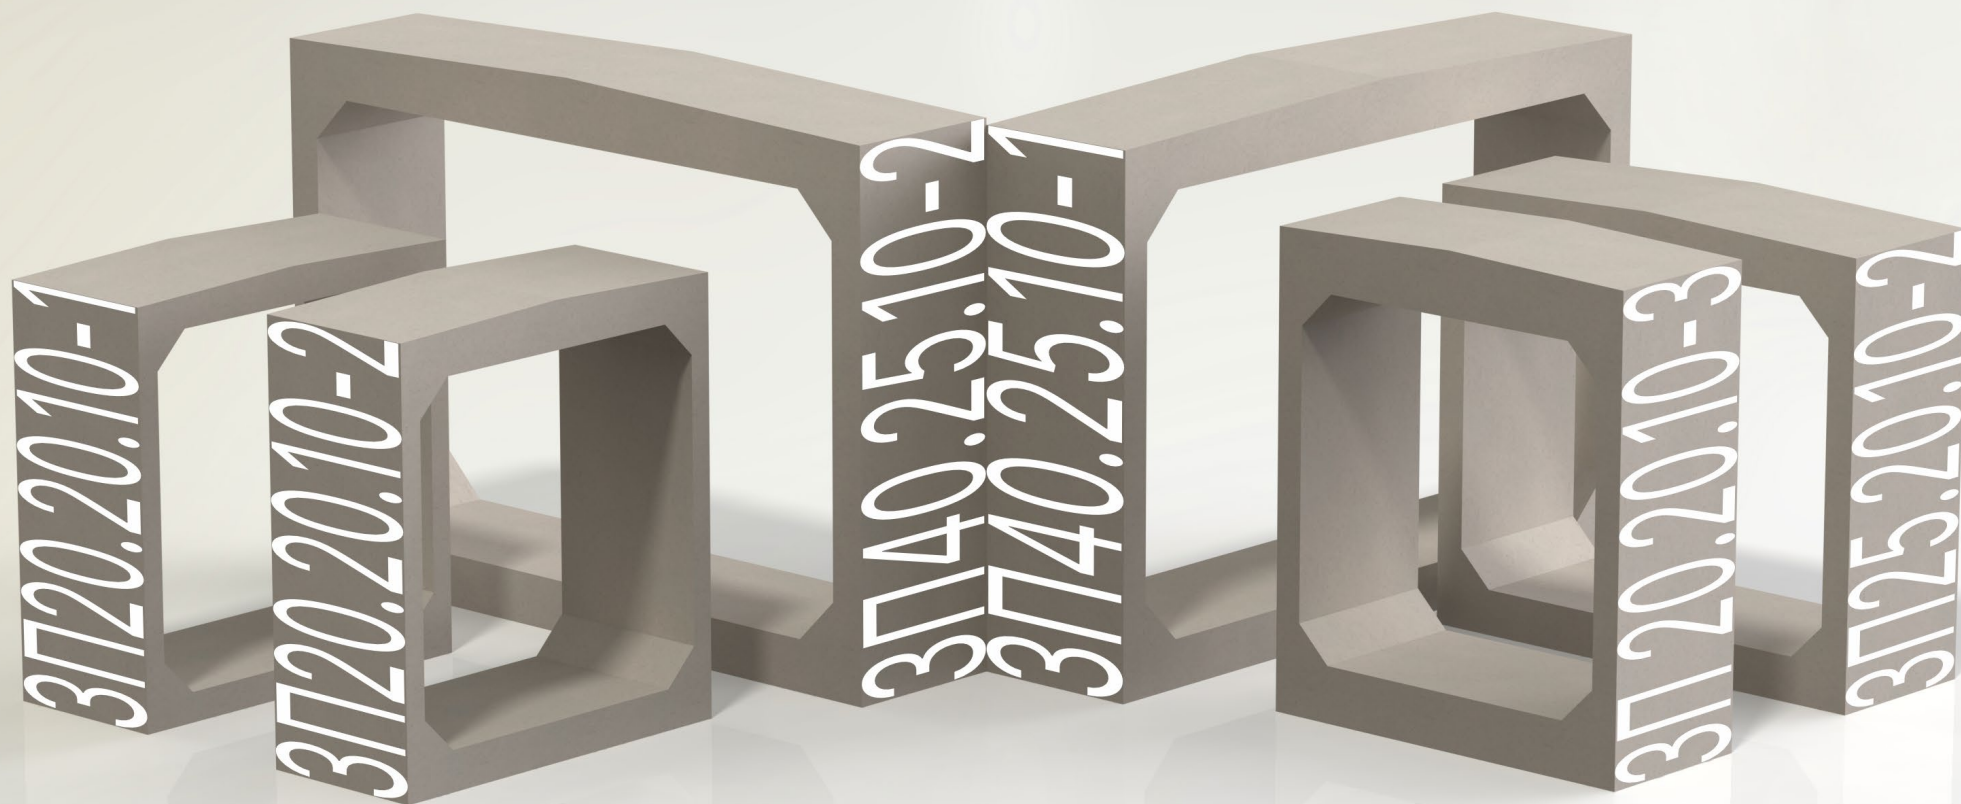

Звенья железобетонные прямо-угольных водопропускных труб под насыпи автомобильных и железных дорог

Габаритные размеры	Марка	Звенья ЗП20.20.10-1 (Б 47)	Звенья ЗП20.20.10-2 (Б 48)	Звенья ЗП25.20.10-2 (Б 50)	Звенья ЗП40.25.10-1 (Б 94)	Звенья ЗП40.25.10-2 (Б 95)	Звенья ЗП 20.20.10-3 (Б 89А)	1
	Длина (mm)	2260	2260	2840	4360	4420	2320	2
	Ширина (mm)	1000	1000	1000	1000	1000	1000	3
	Высота (mm)	2380	2500	2570	3130	3170	2680	4
Размеры отверстия	Ширина (mm)							5
	Высота (mm)							6
Об изделия	Предназначение	Звенья предназначены для устройства периодически действующих и постоянных водотоков под насыпями автомобильных дорог.						7
	Рабочая документация	ТП 3.501:104.UZ Часть 3.Д						8
	Нормативная документация	O'z DSt 3300.1:2018						9
	Технологическая документация	ТИ 02162770-16:2015						10
Свойства	Высота насыпи под автомобильные дороги (m)	5	10	10	6	10	20	11
	Бетон тяжелый	ГОСТ 26633-91						12
	Плотность бетона (kg/m³)	от 2200 до 2500						13
	Класс бетона по прочности на сжатие	В 25						14
	Марка по морозостойкость	F 200						15
	Марка по водонепроницаемости	W 6						16
	Отпускная прочность (%)	80						17
	Объем блока (m³)	1.41	1.69	2.31	3.62	3.98	2.2	18
	Масса звена (t)	3.5	4.2	5.8	9.1	10	5.4	19
Масса арматуры (kg)	Ø6 A240	1.2						20
	Ø8 A240	33.4	33.4	36.5	55.7	51.7		21
	Ø10 A240	34	48	69.6	20.4	21.6		22
	Ø12 A240				102.1	112		23
	Ø14 A240	5.4	5.4					24
	Ø16 A240			7.8				25
	Ø20 A240				15.4			26
	Ø22 A240					19.9	20.14	27
	Ø10 A400	78.8	105.6	101.7	11.2	18.8	221.17	28
	Ø12 A400				147.5			29
	Ø14 A400	35.6						30
	Ø16 A400		66.4			331		31
	Ø20 A400			115.6	183.6			32
	Ø22 A400					270.8	125.16	33
	Общая масса арматуры	188.4	258.8	331.2	535.9	825.8	366.47	34
А	Б	В	Г	Д	Е	Ж	З	




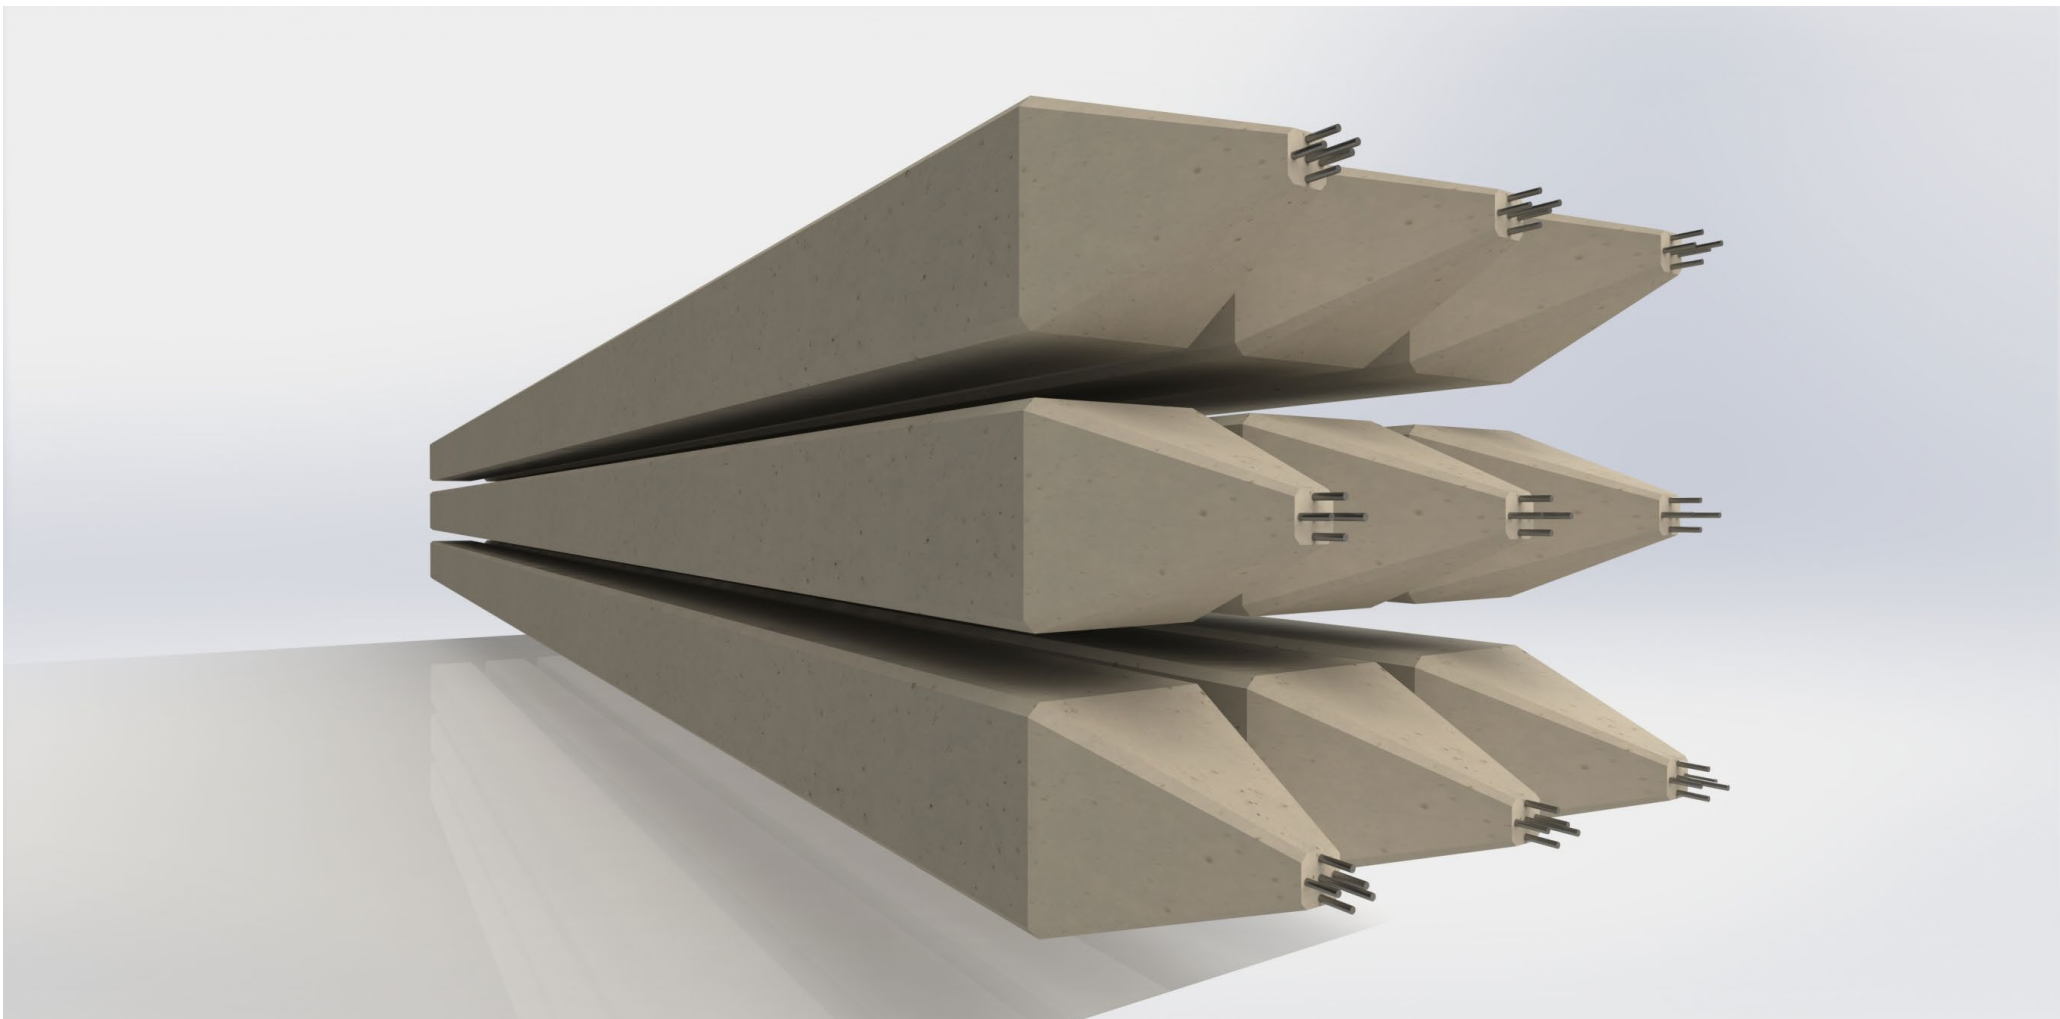

Сваи железобетонные призматические для мостовых опор

№	Марка конструкции	Объем бетона (м³)	Масса (t)	Габаритные размеры (mm)	Класс бетона по прочности на сжатие	Марка по морозостойкости, не менее	Марка по водонепроницаемости, не менее	Плотность бетона (kg/m³)	Нормативная отпускная прочность бетона
<i>A</i>	<i>Б</i>	<i>В</i>	<i>Г</i>	<i>Д</i>	<i>Е</i>	<i>Ж</i>	<i>З</i>	<i>И</i>	<i>К</i>
1	CM 9.35.1 – A400 O'z DSt 3246:2017; CM 9.35.(1T2-5T7) – A400 O'z DSt 3246:2017	1.12	2.80	8000x350x350	B 27.5	F 200	W 6	от 2200 до 2500	100%
2	CM 10.35.1 – A400 O'z DSt 3246:2017; CM 10.35.(1T2-5T7) – A400 O'z DSt 3246:2017	1.25	3.10	10000x350x350					
3	CM 12.35.1 – A400 O'z DSt 3246:2017; CM 12.35.(1T2-5T7) – A400 O'z DSt 3246:2017	1.49	3.70	12000x350x350					
4	CM 14.35.1 – A400 O'z DSt 3246:2017; CM 14.35.(1T3-5T7) – A400 O'z DSt 3246:2017	1.74	4.40	14000x350x350	B 30				




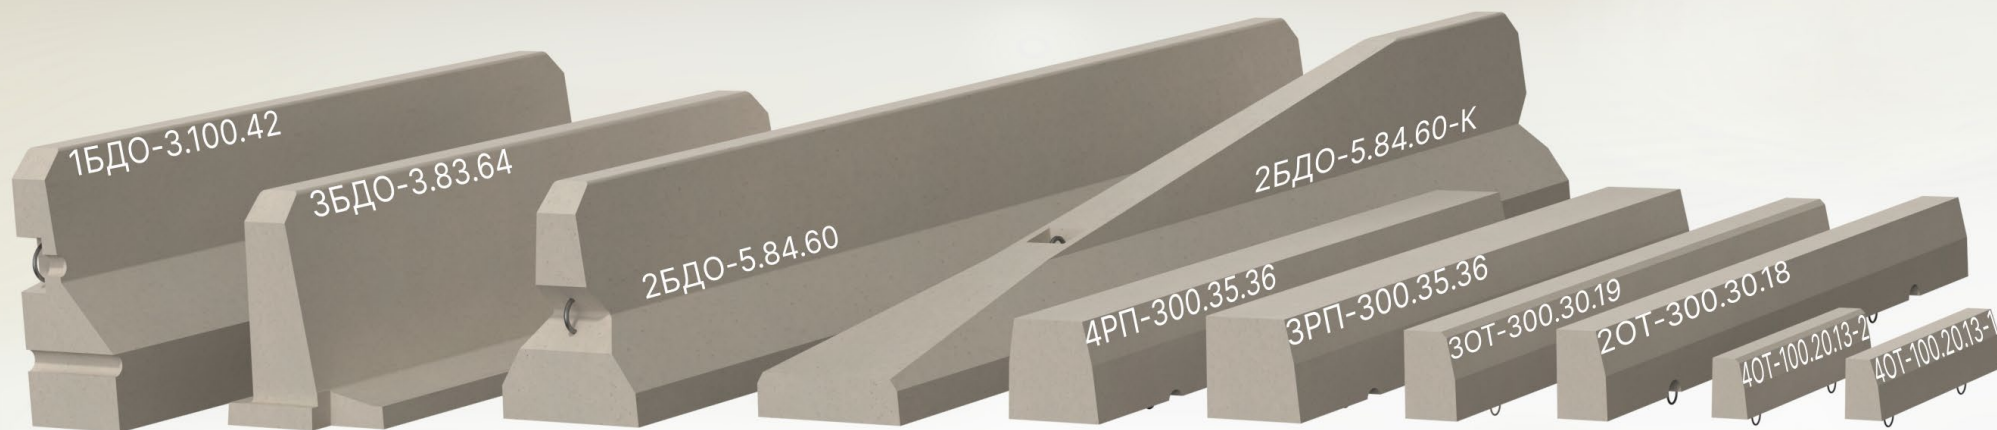

Ограждения барьерного типа и блоки ограждающие

№	Наименование конструкции	Марка конструкции	Обозначение нормативного документа	Объём бетона (м³)	Масса (t)	Габаритные размеры (mm)	Класс бетона по прочности на сжатие	Марка по морозостойкости, не менее	Марка по водонепроницаемости, не менее	Плотность бетона (kg/m³)	Нормативная отпускная прочность бетона, лето/зима (%)
А	Б	В	Г	Д	Е	Ж	З	И	К	Л	М
1	Блоки дорожного ограждения	1БДО-3.100.42-8	О'z DST-3052:2021	0.84	2.10	3000x1000x425	B22,5	F200	W6	2200-2500	70/80
2		1БДО-3.100.42-10									
3		1БДО-3.100.42-12									
4		2БДО-5.84.60-8									
5		2БДО-5.84.60-10									
6		2БДО-5.84.60-12									
7		2БДО-5.84.60-К									
8		3БДО-3.83.64									
9	Блоки ограждения тротуаров	2ОТ-300.30.18		0.15	0.38	3000x300x185	B30	F200	5% по массе, не более	2200-2500	70/80
10		2ОТ-300.30.18-П									
11		3ОТ-100.30.19									
12		3ОТ-200.30.19									
13		3ОТ-300.30.19									
14		3ОТ-300.30.19-П									
15		4ОТ-100.20.13-1									
16		4ОТ-100.20.13-2									
17	Блоки ограждения разделительной полосы	3РП-300.35.36		0.36	0.90	3000x350x365	B30	F200	5% по массе, не более	2200-2500	70/80
18		4РП-300.35.36									




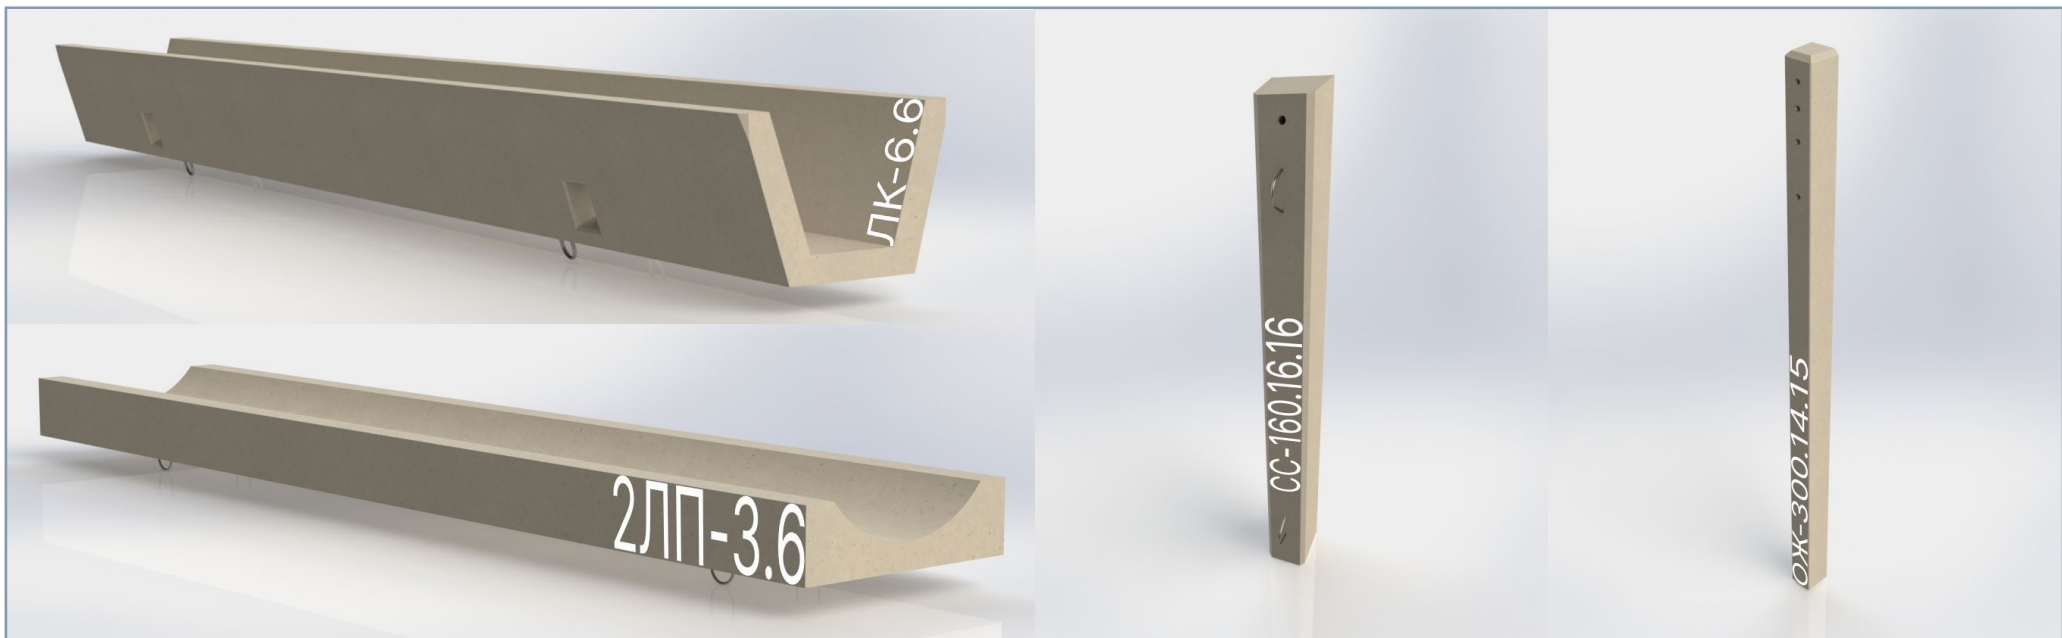

Лотки кюветные, прикромочные, сигнальный столбик и ж/б опоры дорожных знаков


№	Наименование конструкции	Марка конструкции	Обозначение нормативного документа	Объём бетона (м³)	Масса (t)	Габаритные размеры (mm)	Класс бетона по прочности на сжатие	Марка по морозостойкости, не менее	Марка по водонепроницаемости, не менее	Плотность бетона (kg/m³)	Нормативная отпускная прочность бетона, лето/зима (%)
А	Б	В	Г	Д	Е	Ж	З	И	К	Л	М
1	Лотки	ЛК-6.6	О'z DSt-3028:2021	0.55	1.38	6000x380/630x470	B22,5	F150	W4	2200-2500	80
2	железобетонные	ЛК-3.6		0.28	0.69	3000x380/630x470					
3	кюветные	ЛК-2.6		0.18	0.46	2600x380/630x470					
4		ЛК-1.6		0.09	0.23	1600x380/630x470					
5		ЛК-0,5.6		0.05	0.12	500x360/610x440					
6		ЛК-0,5.6		0.05	0.12	500x380/630x470					
7	Лотки	2ЛП-3.6		0.19	0.47	3000x570x160					
8	железобетонные	2ЛП-2.6		0.12	0.31	2000x570x160					
9	прикромочные	2ЛП-1.6		0.06	0.16	1000x570x160					
10		2ЛП-0,5.6		0.03	0.08	500x570x160					
11	Столбик сигнальный	СС-160.16.16	ОЖ-300.14.15	0.04	0.09	1600x160x160 (высота, длина, ширина)	B30	F100	W2	2200-2500	70/80
12	Опоры железобетонные дорожных знаков	ОЖ-300.14.15		0.06	0.15	3000x140x130/150 (высота, длина, ширина)	B15	F100	W2	2200-2500	70/80
13		ОЖ-400.14.15		0.08	0.21	4000x140x130/150 (высота, длина, ширина)					



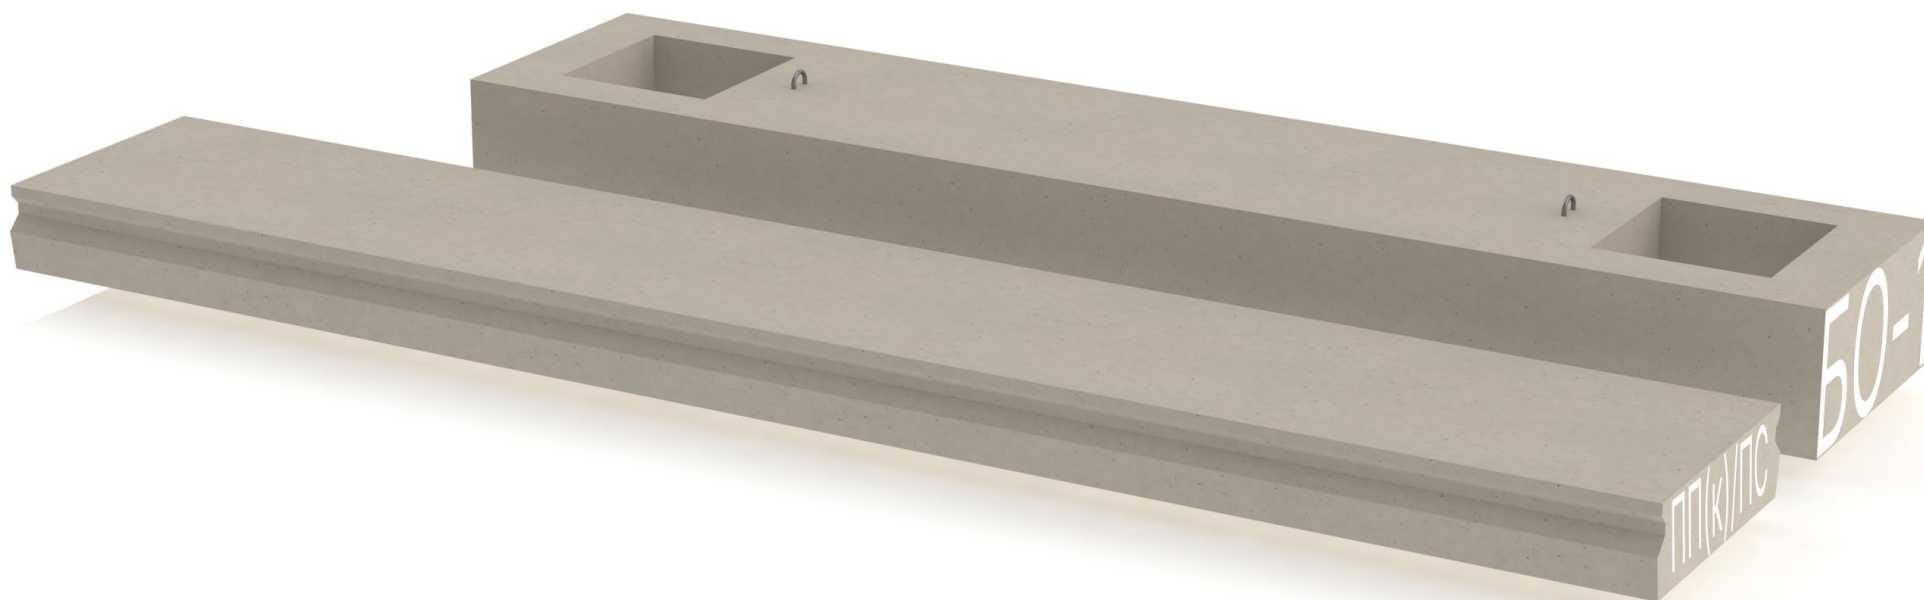


№	Наименование конструкции	Марка конструкции	Обозначение нормативного документа	Объём бетона (м³)	Масса (t)	Габаритные размеры (mm)	Класс бетона по прочности на сжатие	Марка по морозостойкости, не менее	Марка по водонепроницаемости, не менее	Плотность бетона (kg/m³)	Нормативная отпускная прочность бетона, лето/зима (%)
А	Б	В	Г	Д	Е	Ж	З	И	К	Л	М
1	Плиты	ПП (к) 8.99.45	О'z DSt-3026:2021	3.30	8.25	8000x990/940x450	B27,5	F 200	W6	2200-2500	80
2	железобетонные	ПП (к) 6.99.30		1.69	4.23	6000x990/940x300					
3	переходные	ПП (к) 5.99.30		1.42	3.55	5000x990/940x300					
4		ПП (к) 4.99.30		1.13	2.80	4000x990/940x300					
5		ПП (к) 3.99.30		0.85	2.13	3000x990/940x300					
6		ПП (к) 3.200.24		1.44	3.60	3000x2000x240					
7	Плиты железобетонные мостовые сплошного сечения с ненапрягаемой арматурой	ПС 6.99.30		1.69	4.23	6000x940x300	B22,5	F200	W6		80
8	Блоки железобетонные опор мостов	БО 1-5.100.49		2.10	5.25	5000x1000x490					



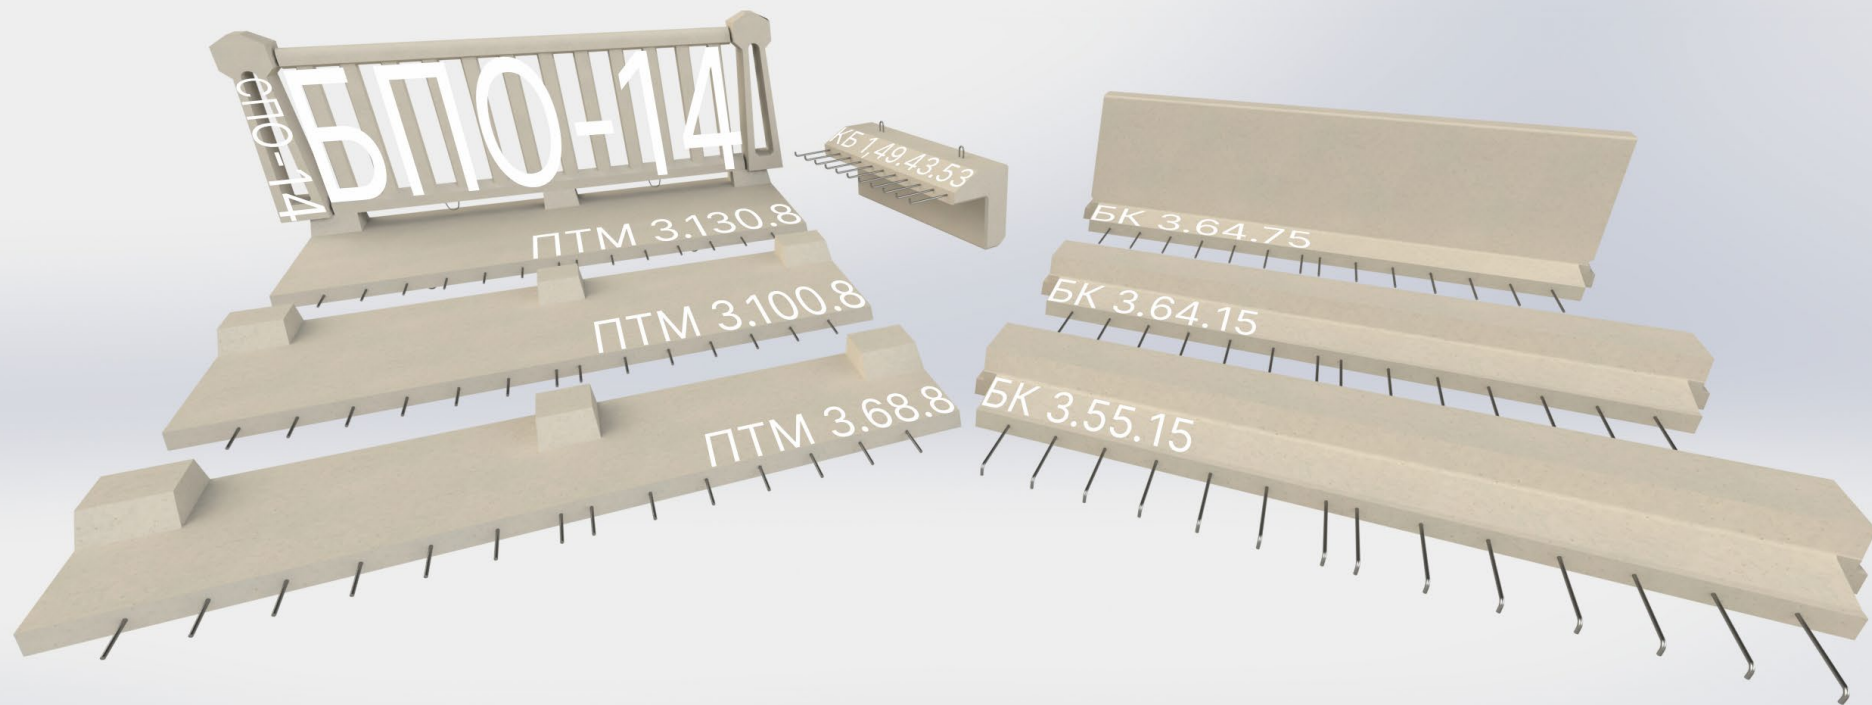

№	Наименование конструкции	Марка конструкции	Обозначение нормативного документа	Объём бетона (м³)	Масса (t)	Габаритные размеры (mm)	Класс бетона по прочности на сжатие	Марка по морозостойкости, не менее	Марка по водонепроницаемости, не менее	Плотность бетона (kg/m³)	Нормативная отпускная прочность бетона, лето/зима (%)
А	Б	В	Г	Д	Е	Ж	З	И	К	Л	М
1	Блок железобетонный перильного ограждения	БПО-14	O'z MSt 202	0.05	0.13	1330x120x1010	B30	F200	W6	2150	70/90
2		СПО-14		0.03	0.08	300x160x1135	B22,5			2400	
3	Блок колесоотбойный составного тротуарного блока	БК 3.55.75	O'z DSt-3026:2021	0.65	1.63	2990x550x750	B35	F200	W6	2200-2500	70/90
4		БК 3.55.15		0.26	0.65	2990x550x150					
5		БК 3.64.15		0.28	0.70	2990x640x150					
6		БК 3.64.75		0.69	1.70	2990x640x750					
7		БК 3.79.75		0.71	1.78	2990x680x80					
8	Плита тротуарная мостовая составного тротуарного блока	ПТМ 3.68.8	O'z DSt-3026:2021	0.18	0.46	2990x680x80	B35	F200	W6	2200-2500	70/90
9		ПТМ 3.100.8		0.26	0.65	2990x1000x80					
10		ПТМ 3.130.8		0.38	0.95	2990x1300x80					
11	Карнизный блок	КБ 1,49.43.53	O'z DSt-3026:2021	0.19	0.47	1490x430x530	B35	F200	W6	2200-2500	70/90



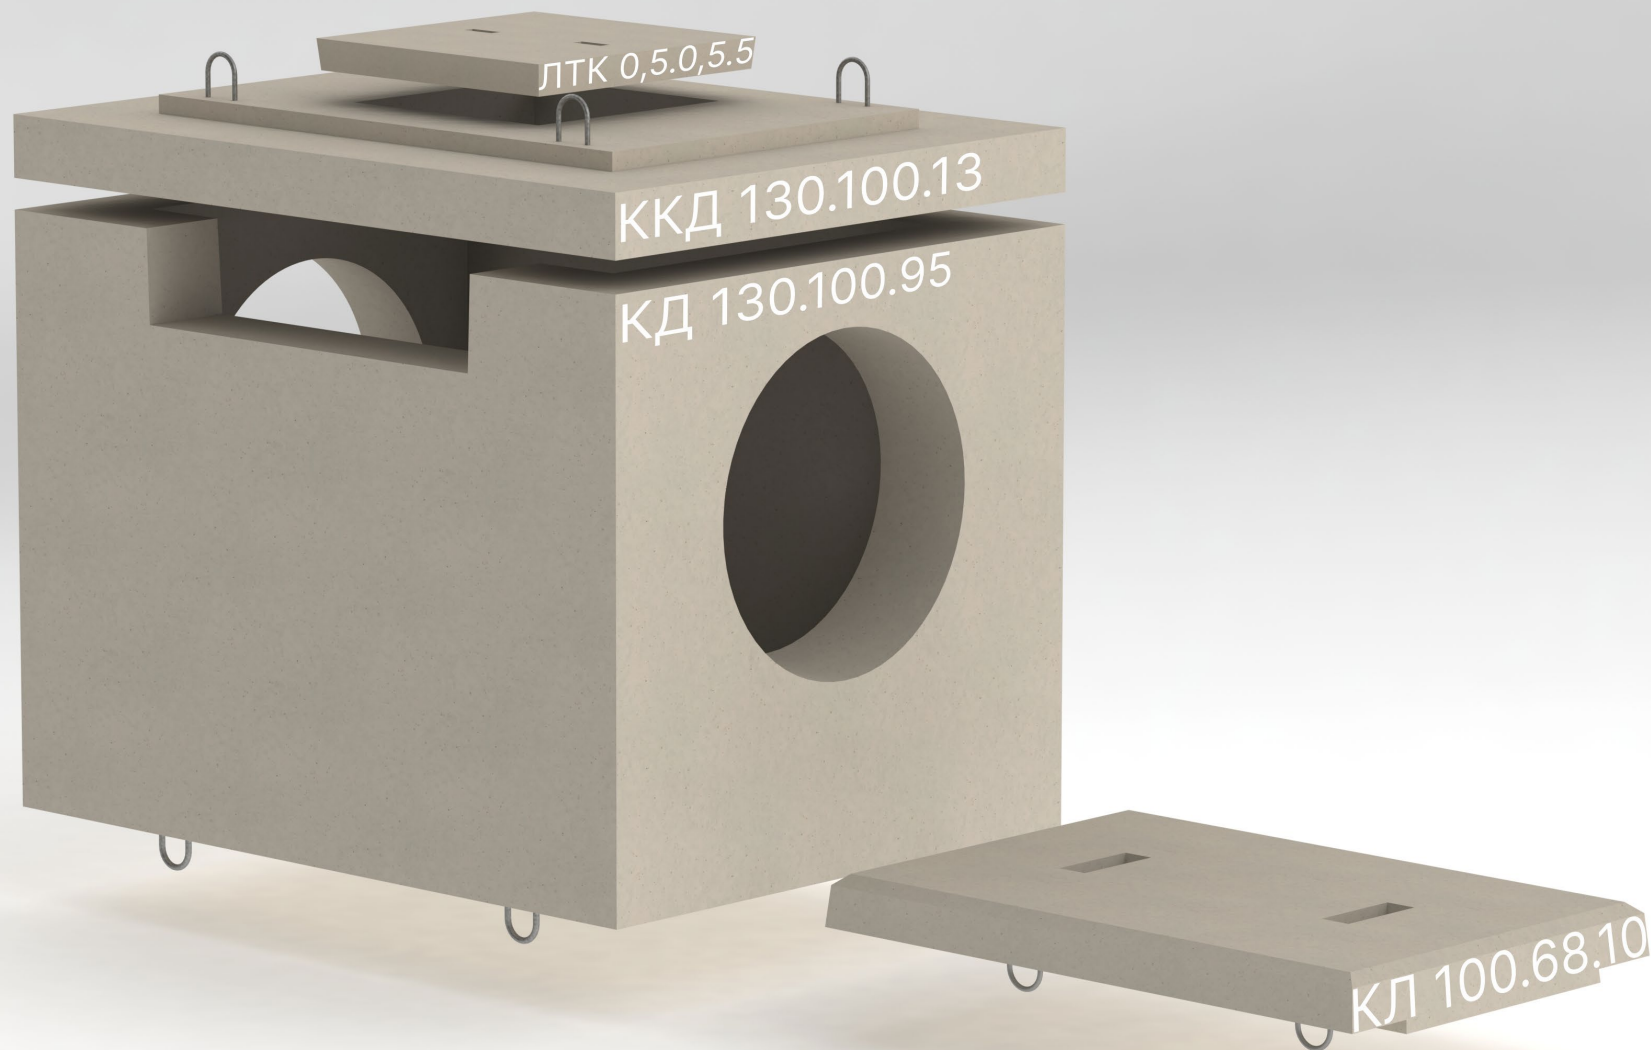

№	Наименование конструкции	Марка конструкции	Обозначение нормативного документа	Объём бетона (м³)	Масса (т)	Габаритные размеры (мм)	Класс бетона по прочности на сжатие	Марка по морозостойкости, не менее	Марка по водонепроницаемости, не менее	Плотность бетона (кг/м³)	Нормативная отпускная прочность бетона, лето/зима (%)
А	Б	В	Г	Д	Е	Ж	З	И	К	Л	М
1	Колодец железобетонный дренажный	КД 130.100.95	ГОСТ 13015-2012	0.65	1.63	1300x1000x950	В22,5	F200	W6	2200-2500	80
2	Крышка железобетонная колодца дренажного	ККД 130.100.13		0.14	0.35	1300x1000x130					
3	Люк железобетонный крышки колодца	ПТК 0,5.0,5.5		0.01	0.03	500x500x50					
4	Крышка железобетонная лотка ЛК	КЛ 100.68.10		0.06	0.16	1000X680X100					



№	Наименование конструкции	Марка конструкции	Обозначение нормативного документа	Объём бетона (м³)	Масса (t)	Габаритные размеры (mm)	Класс бетона по прочности на сжатие	Марка по морозостойкости, не менее	Марка по водонепроницаемости, не менее	Плотность бетона (kg/m³)	Нормативная отпускная прочность бетона, лето/зима (%)
А	Б	В	Г	Д	Е	Ж	З	И	К	Л	М
1	Блоки железобетонные подпорной стенки переменной высоты от 15 до 90 дм	Типа БПС (геометрия)	O'z DSt-3026:2021	По чертежам заказчика	По чертежам заказчика	По чертежам заказчика	B 25	F200			
2	Ригели железобетонные типа Р	Р (геометрия)	O'z DSt-3026:2021				B25	F200			
3	Лежни железобетонные типа Л	Л (геометрия)	O'z DSt-3026:2021				B22,5	F200			
4	Плита железобетонная разделительной полосы типа ПРП	ПРП (геометрия)	O'z DSt-3026:2021				B27,5	F200			
5	Плиты железобетонные декоративные типа ПД	ПД (геометрия)	O'z DSt-3026:2021				B30	F200	W4	2200-2500	90
6	Стойки железобетонные вертикальные и наклонные типа СВ и типа СН	СВ (геометрия) СН (геометрия)	O'z DSt-3026:2021 O'z DSt-3026:2021				1-я группа B25 2-я группа B27,5	F200	W6	2200-2500	100
7	Фундаменты железобетонные типа Ф	Ф (геометрия)	O'z DSt-3026:2021				1-я группа B15 2-я группа B22,5 3-я группа B25	F150 F200 F200	W4 W6 W6	2200-2500	

Примечание

- Каталог не является источником информации по которому можно руководствоваться при изготовлении изделий. Изделия производятся строго соблюдая нормативно-технологические документы и чертежи. Каталог служит только в ознакомительных целях.
- Все иллюстрации и фото-рендеры сгенерированы только для ознакомления. При использовании фото-материалов каталога необходимо указать ссылку на источник.
- Каталог создан на основе обновленного файла Номенклатура. В случае конфликта информации полагаться на файл Номенклатура. Файл Номенклатура так же доступен на сайте www.uzyulkuprik.uz
- Примечание: Для изделий «Конструкций по чертежам заказчика» класс бетона справочный. На каждое транспортное сооружение класс бетона должен указываться в чертежах Заказчика, утверждённым в установленном порядке.
- Каталог состоит из 17 страниц.
- Адрес: ГУ кластер «Ўзйўлкўприк», г. Ташкент, Яшнободский р-н, Уртамасжид МФЙ, ул. Оханграбо, д. 12, 100146
- Контакты: тел.: +998 55 515 16 16; эл-почта: ozyolkoprik@gmail.com;
- Новый вид(данный) каталога был создан начальником отдела инновации и цифровизация, Маликовым Ф. Ф. в 2024 году.

